


PROPOSED ROUTE KEYPLAN FOR Koyalibeda block (Pakhanjore Block)
RING-3 LENGTH 77.556 KMS+ (SPUR+RING PROTECTION) LENGTH =23.674 KMS
TOTAL LENGTH 101.230 KMS

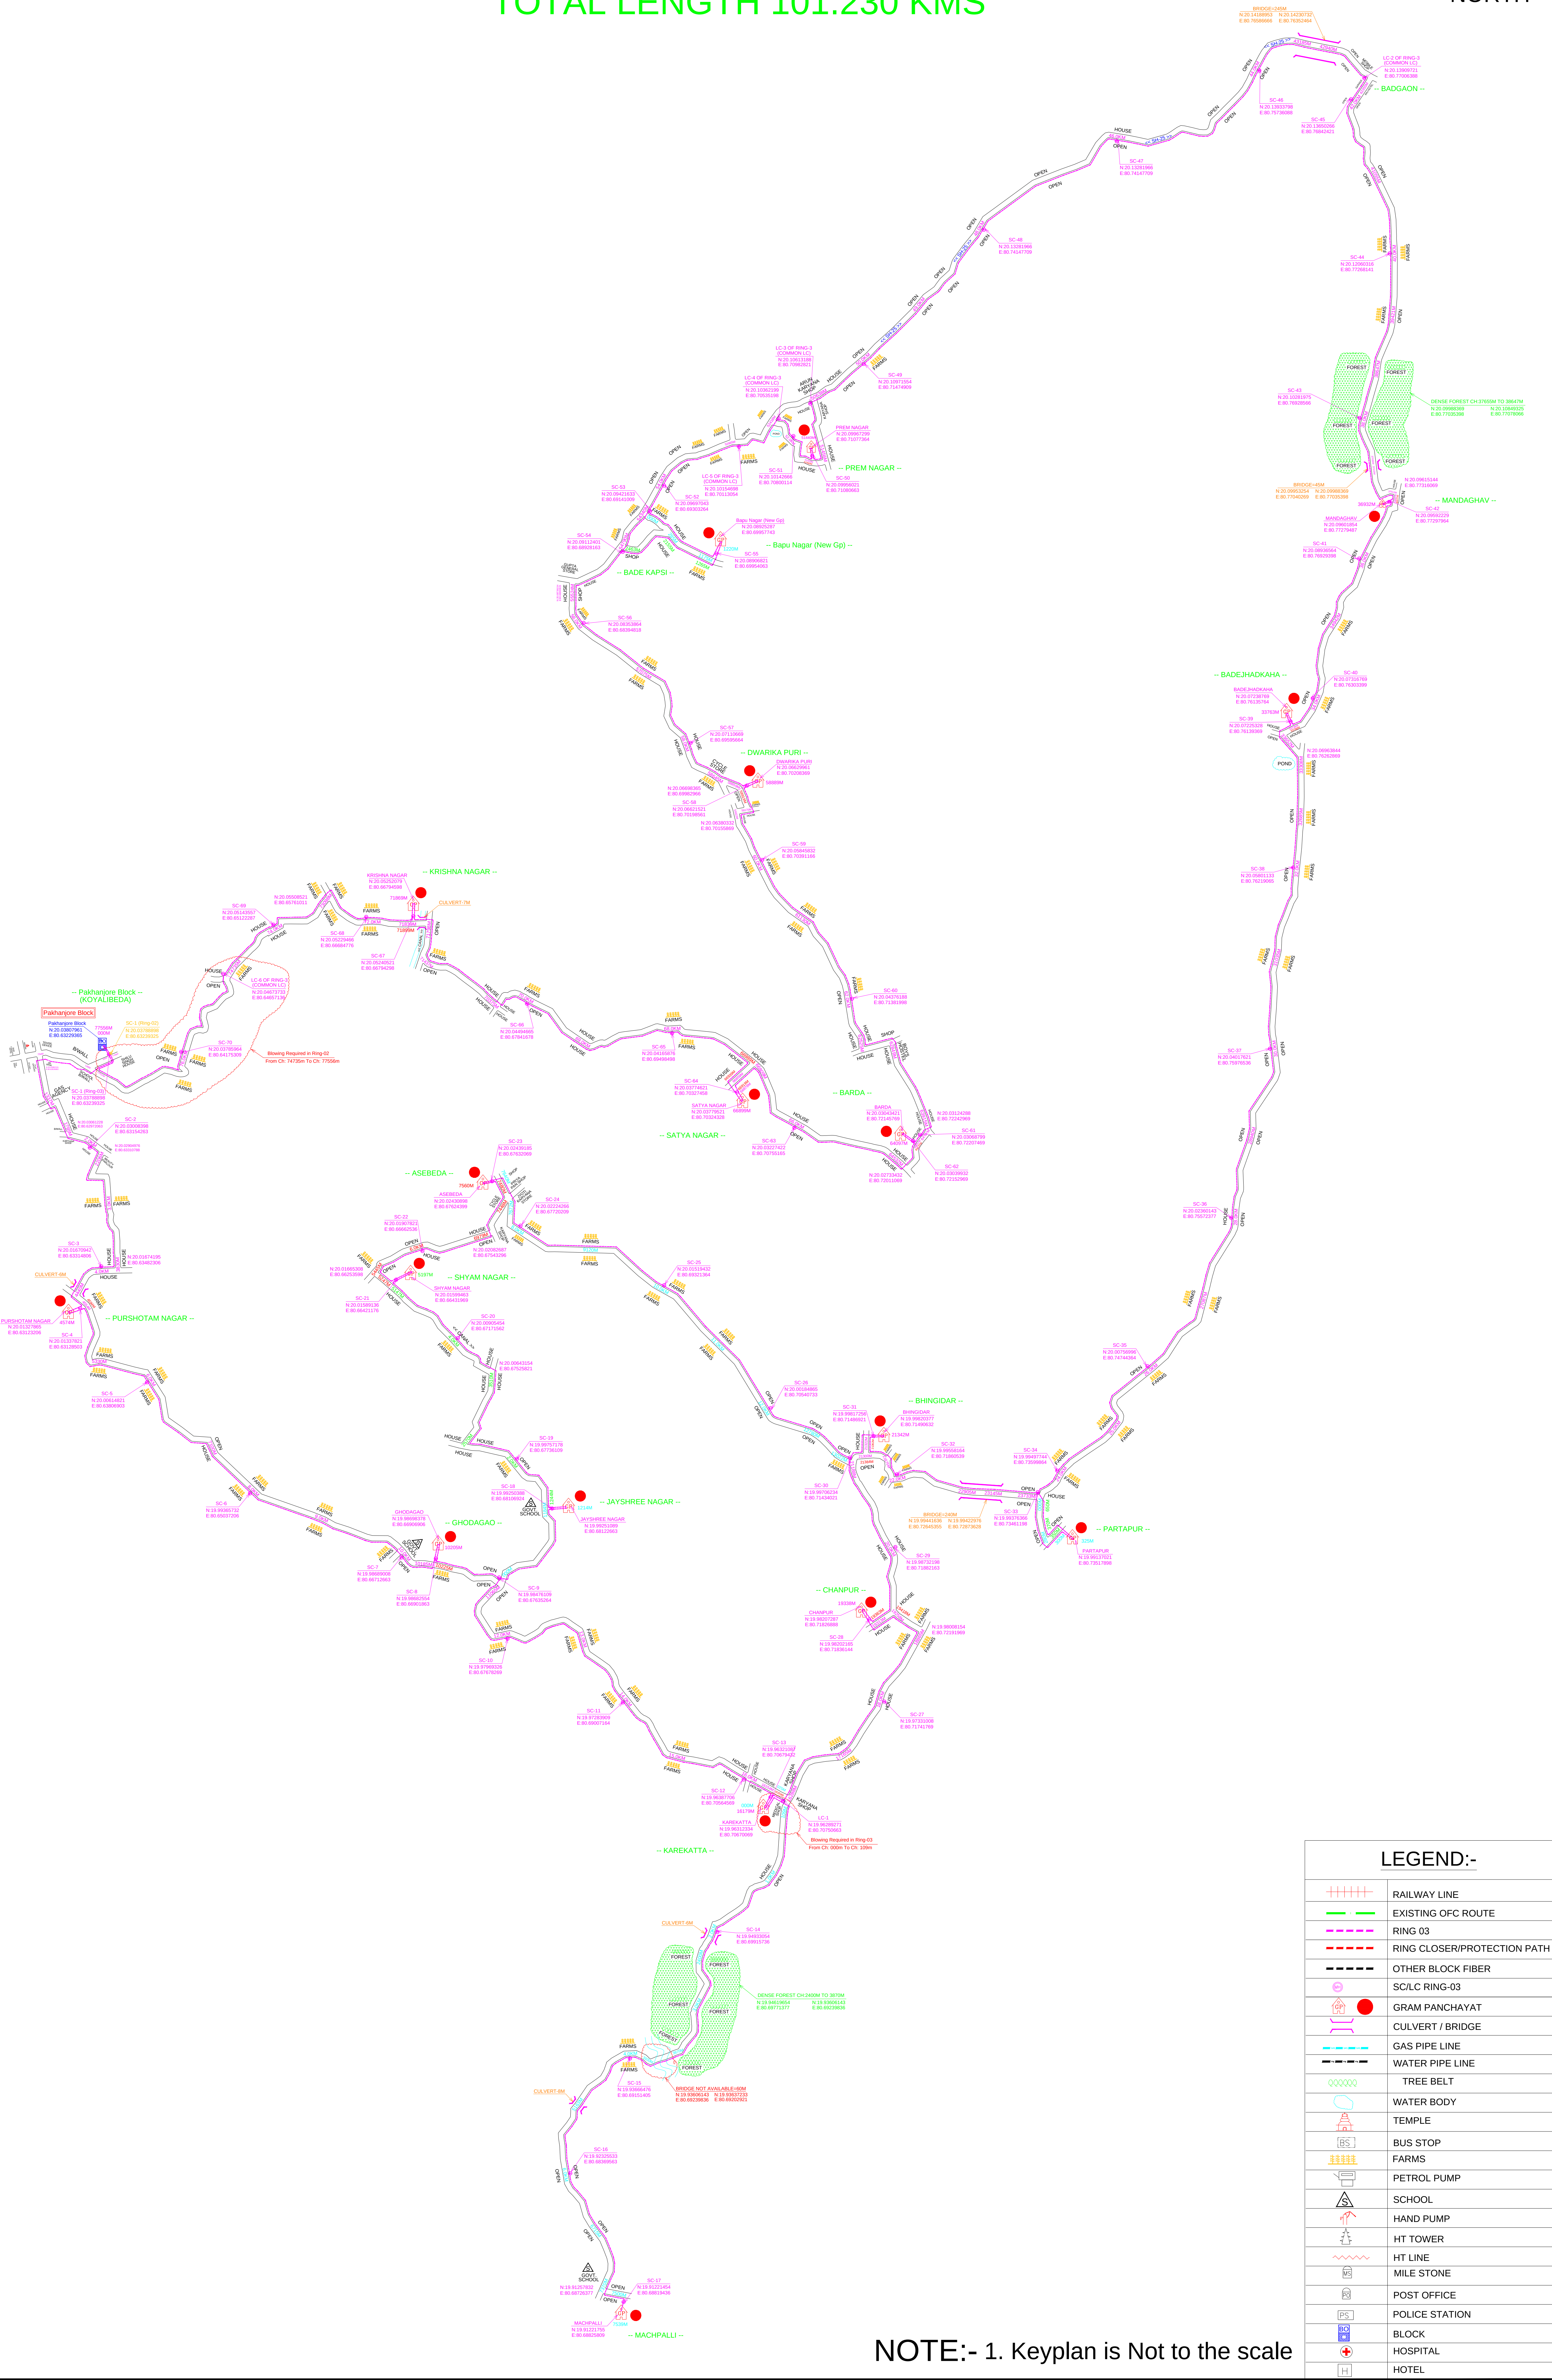

LEGEND:-

+++++	RAILWAY LINE
---	EXISTING OFC ROUTE
---	RING 03
---	RING CLOSER/PROTECTION PATH
---	OTHER BLOCK FIBER
○	SC/LC RING-03
●	GRAM PANCHAYAT
⌋	CULVERT / BRIDGE
---	GAS PIPE LINE
---	WATER PIPE LINE
○○○○○	TREE BELT
○	WATER BODY
⌋	TEMPLE
⌋	BUS STOP
⌋	FARMS
⌋	PETROL PUMP
⌋	SCHOOL
⌋	HAND PUMP
⌋	HT TOWER
⌋	HT LINE
⌋	MILE STONE
⌋	POST OFFICE
⌋	POLICE STATION
⌋	BLOCK
⌋	HOSPITAL
⌋	HOTEL

NOTE:- 1. Keyplan is Not to the scale